CONSTRUCTION NOTES.

STANDARD NOTES FOR THE CONSTRUCTION OF THIS DWELLING TO BE APPLIED TO THE SUBSEQUENT DOCUMENTATION PAGES.

1. GENERAL.

1.1 © COPYRIGHT - REPRODUCTION IN PART OR WHOLE IS STRICTLY FORBIDDEN.
1.2 DO NOT SCALE PLANS. USE WRITTEN DIMENSIONS ONLY.
1.3 VERIFY ALL DIMENSIONS PRIOR TO ORDERING OR SHOP FABRICATION.
1.4 N.C.C. REFERS TO NATIONAL CONSTRUCTION CODE OF AUSTRALIA.
1.5 AS. REFERES TO AUSTRALIAN STANDARDS.
1.6 ALL BUILDING WORKS CONFORM TO THE N.C.C., AS CODES (CURRENT EDITIONS), BUILDING REGULATIONS, LOCAL BY-LAWS AND TOWN PLANNING REQUIREMENTS.
1.7 THESE PLANS SHALL BE READ IN CONJUCTION WITH ANY STRUCTURAL OR CIVIL ENGINEERING COMPUTATIONS AND DRAWINGS.
1.8 ALL CEILING PENETRATIONS INCLUDING ITEMS SUCH AS INTERNAL ROOF ACCESS, EXHAUST FANS AND HEATING DUCTS ARE APPROXIMATE AND MAY BE ADJUSTED DUE TO ROOF TRUSS POSITIONS.

2. FOOTINGS.

2.1 REFER TO ENGINEERING DESIGN FOR ALL SLAB AND FOOTING DETAILS AS PER AS2870.
2.2 NO PART OF FOOTINGS TO ENCROACH TITLE BOUNDARIES AND EASEMENT LINES.

3. SITE.

3.1 PROVIDE TEMPORARY FENCING (AS PER COUNCIL REQUIREMENTS).
3.2 ESTABLISHMENT OF SITE BOUNDARIES IS THE RESPONSIBILITY OF THE OWNER/S.

4. DRAINAGE.

4.1 STORMWATER DRAINAGE TO DISCHARGE TO LEGAL POINT AS PER LOCAL AUTHORITIES.
4.2 ALL STORMWATER TRENCHES WITHIN 1.5m OF THE BUILDING ARE REQUIRED TO BE BACK FILLED WITH CLAY TO THE TOP 300mm.
4.3 THE GROUND SURFACE SHALL BE GRADED AWAY FROM THE SLAB TO A MINIMUM 1:20 TO ENSURE DRAINAGE OF SURFACE WATER AWAY FROM THE BUILDING AREA AS PER AS2870.
4.4 TEMPORARY DOWNPIPES (SOCKS) TO BE USED DURING THE CONSTRUCTION PERIOD.
4.5 HWS OVERFLOW AND SURFACE DRAINS TO BE CONNECTED INTO STORMWATER AND DIRECTED TO CONNECTION VIA 100mm PVC PIPES AS PER LOCAL AUTHORITIES' REQUIREMENTS.
4.6 DOWNPIPES TO BE LOCATED MAXIMUM 12m APART. GUTTERS SLOTTED TO MAKE PROVISION OF OVERFLOWS AS PER N.C.C. PART 3.5.2.
4.7 MAXIMUM STEP DOWN TO PORTICO, ALFRESCO, GARAGE, BALCONY OR THE LIKE TO NOT EXCEED 190mm AND A MINIMUM OF 50mm.

5. BRICKWORK.

5.1 ALL BRICKWORK TO BE IN ACCORDANCE WITH AS3700 AND AS4773.1.
5.2 UNREINFORCED MASONRY IS TO COMPLY WITH N.C.C. REQUIREMENTS PART 3.3.1.
5.3 PROVIDE WALL TIES TO BRICKWORK AT MAXIMUM 600mm CENTERS IN EACH DIRECTION AND WITHIN 300mm OF ARTICULATION JOINTS.

6. TIMBER.

6.1 ALL FRAMING TO BE IN ACCORDANCE WITH AS1684.
6.2 ALL TIE DOWN, CONNECTIONS AND BRACING SHALL COMPLY WITH AS1664.

7. ROOF.

7.1 ALL PLUMBING AND DRAINAGE WORKS TO COMPLY WITH AS3500.

8. THERMAL PERFORMANCE.

8.1 R4.1 BATT INSULATION TO CEILING (EXCLUDING GARAGE).
8.2 R2.5 BATTS PLUS WALL WRAP TO ALL EXTERNAL HOUSE WALLS.
8.3 R2.5 BATTS TO HOUSE/GARAGE COMMON WALL.
8.4 BUILDING FABRIC THERMAL INSULATION TO COMPLY WITH N.C.C. 3.12.1.1.
8.5 THERMAL INSULATION MUST FORM A CONTINUOUS BARRIER WITH CEILINGS AND WALLS CONTRIBUTING TO THE THERMAL BARRIER. INSULATION TO ABUT OR OVERLAP ADJOINING INSULATION OTHER THAN BEING INTERUPTED BY A STRUCTURAL MEMBER.
8.6 BULK INSULATION TO BE INSTALLED SO THAT IT MAINTAINS IT THICKNESS.
8.7 EXHAUST FANS WITH SELF CLOSING DAMPER.
8.8 CSR INSPECTION & CERTIFICATION INCLUDING TAPED WALL WRAP TO JOINS, ALL PENETRATIONS & POLYESTER STRIP SEAL TO ALL WINDOWS & DOORS AS PER N.C.C. PART 3.12.3."
8.9 WINDOWS COMPLY WITH AS 2047 FOR AIR INFILTRATION AS REQUIRED BY N.C.C. 3.12.3.3.
8.10 REFER TO THERMAL PERFORMANCE ASSESSORS REPORT FOR WINDOW FRAME AND GLAZING SPECIFICATION.
8.11 WEATHERSTRIP DRAFT PROTECTION DEVICE TO BOTTOM OF EXTERNAL HINGED DOORS WITH SEALS TO HEADS AND JAMBS. (EXCLUDES GARAGE REAR ACCESS DOOR IF SHOWN ON PLAN).
8.12 DUCT WORK TO COMPLY WITH N.C.C. 3.12.5.3 FOR HEATING AND COOLING.

9. WET AREAS.

9.1 LIFT OFF HINGED DOOR TO WC's WHEN DOOR SWING IS WITHIN 1200mm OF TOILET PAN.
9.2 EXHAUST FANS COMPLYING WITH AS1668.2 TO BE INSTALLED AS PER N.C.C. PART 2.4.5.
9.3 30mm GAP TO THE BOTTOM OF DOORS IN WET AREAS WHERE EXHAUST FAN IS INSTALLED.
9.4 WATERPROOFING OF ALL WET AREAS TO BE IN ACCORDANCE WITH AS3740. WALL FINISHES SHALL BE IMPERVIOUS TO A HEIGHT OF 1800mm ABOVE FLOOR LEVEL TO SHOWER ENCLOSURES AND 300mm ABOVE BATHS, BASINS, SINKS AND LAUNDRY TROUGHS IF WITHIN 75mm OF THE WALL.

10. WINDOWS.

10.1 ALL GLAZING TO BE IN ACCORDANCE WITH AS1288.
10.2 LOWLITE WINDOWS TO HAVE 5mm ANNEALED OR SAFETY GLAZING.
10.3 WINDOWS WITHIN 300mm FROM AN OPENING OR DOORWAY TO BE SAFETY GLAZED.
10.4 WINDOW SIZES ARE GENERALLY SHOWN NOMINAL, ACTUAL SIZE WILL VARY ACCORDING TO MANUFACTURER. WINDOWS TO BE FLASHED ALL AROUND.
10.5 LIGHT AND VENTILATION MUST BE PROVIDED TO ALL HABITABLE ROOMS AS PER THE N.C.C. PART 3.8.4 AND PART 3.8.5.
10.6 PROVIDE RESTRICTIVE WINDERS OF 125mm MAX TO ALL OPENABLE BEDROOM WINDOWS WHERE THE FLOOR BENEATH IS MORE THAN 2m ABOVE SURFACE BENEATH.
10.7 SAFETY GLASS TO BE USED IN THE FOLLOWING CASES:
i) ALL ROOMS - WITHIN 500mm VERTICAL OF THE FLOOR.
ii) BATHROOMS - WITHIN 2000mm OF THE FLOOR.
iii) LAUNDRY - WITHIN 1200mm VERTICAL FROM FLOOR AND/OR WITHIN 300mm HORIZONTAL FROM ALL DOORS.
iv) DOORWAY - WITHIN 300mm HORIZONTAL FROM DOORS.

11. SMOKE ALARMS.

11.1 SMOKE ALARMS INTERCONNECTED AND COMPLYING WITH AS3786 ARE TO BE INSTALLED IN ACCORDANCE WITH N.C.C. PART 3.7.2.

SITE SPECIFIC NOTES

SITE SPECIFIC NOTES FOR THE CONSTRUCTION OF THIS DWELLING TO BE APPLIED TO THE SUBSEQUENT DOCUMENTATION PAGES.

TERMITE

- TERMITE PROTECTION TO BE IN ACCORDANCE WITH N.C.C. PART 3.1.3 AND AS3660.1
- PART A TERMITE PROTECTION TO THE DWELLING WITH COLLARS TO SLAB PENETRATIONS
- STAINLESS STEEL MESH TO WALLS ON BOUNDARY
- TIMBER POSTS TO BE SOLID PIN STIRRUPS WITH 75mm CLEARENCE TO GROUND SURFACE

WALL ON BOUNDARY.

- EXTERNAL WALLS ON BOUNDARY ARE TO BE CONSTRUCTED TO N.C.C. 3.7.1 WITH NON COMBUSTIBLE MATERIAL TO UNDERSIDE OF ROOFING MATERIAL.
- EAVE NEAR SITE BOUNDARY IS TO BE PROTECTED FROM THE SPREAD OF FIRE IN ACCORDANCE WITH N.C.C. 2.3.1 BY THE ROOFING MATERIAL, GUTTER AND EAVE LINING ALL NON COMBUSTIBLE.
- WALLS ON OR WITHIN 900mm FROM SITE BOUNDARIES ARE TO BE FRL 60/60/60.

BAL - 12.5

BUSHFIRE ATTACK LEVEL INCLUSIONS

* CONSTRUCTION TO COMPLY WITH AS3959 CONSTRUCTION OF BUILDINGS IN BUSHFIRE PRONE AREAS.
* SARKING TO ENTIRE ROOF INCLUDING COVERING OF RIDGE & EXTENDING INTO GUTTERS AND VALLEYS (RP-81).
* ROOF VENT (WHIRLY BIRD) REQUIRED WITH MESH EMBER GUARD.
* FLASHINGS TO BE NON COMBUSTIBLE.
* TILED ROOF TO HAVE ANTI-PONDING BOARDS.
* EMBER GUARDS TO VENT PIPES AND ROOF VENTILATORS.
* NON COMBUSTIBLE SEALANT TO ALL ROOF PENETRATIONS.
* EAVES LINING 4.5mm FIBRE CEMENT SHEETING.
* 4.5mm FIBRE CEMENT SHEET ABOVE WINDOWS/DOORS WHERE INDICATED ON ELEVATIONS.
* ALUMINIUM MESH FLYSCREENS WITH MAX. 2mm APERTURE TO ALL OPENINGS.
* ALL WALLS NOT TO HAVE A GAP GREATER THAN 3mm.
* 4mm GRADE A SAFETY FOR ANY GLAZING LESS THAN 400mm ABOVE GROUND.
* ENTRY DOORS FROM SELECT RANGE OF FIRE PRONE AREA DOORS ONLY.
* VICTORIAN ASH KDHW TIMBER DOOR FRAMES.
* RP4 SEALS TO EXTERNAL PERIMETER HINGED DOORS.
* RP59 SEAL TO REAR GARAGE DOOR.
* GARAGE VEHICLE ACCESS DOOR FITTED WITH NYLON BRISTLE BRUSH SEAL OR EQUIVALENT AND SEAL TO BOTTOM OF DOOR.
* SPARK ARRESTORS TO ALL WEEP HOLES MAX. APERTURE 2mm.
* WATER AND GAS SUPPLY PIPES TO BE METAL WHEN ABOVE GROUND.
* EVAPORATIVE COOLERS TO BE BAL COMPLIANT.

Education Only

Builder

PROPOSED RESIDENCE FOR OWNER/S


ADDRESS

MODEL L

TITLE NOTES

SPEC

MAP | JOB NO | DRN | MST | SCALE | SHEET 1 OF 12

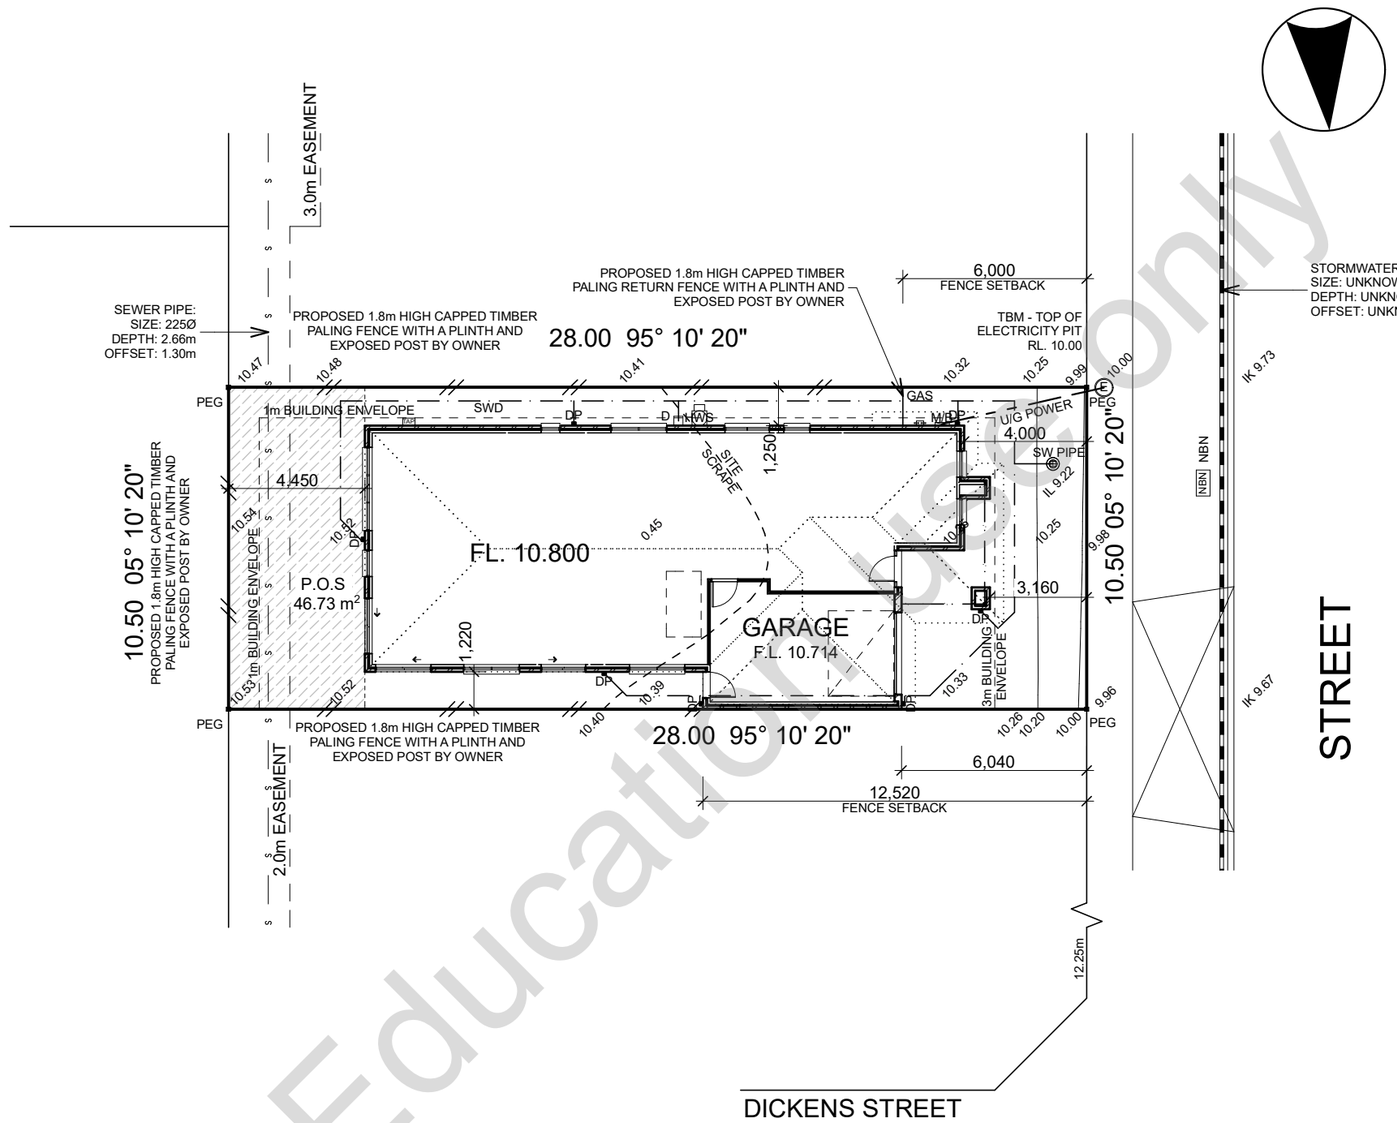

SITE NOTES

- WAFFLE RAFT SLAB TO ENGINEERS' DESIGN ON MAXIMUM 50mm LEVELLED CRUSHED ROCK BASE.
- 400mm MIN. FREEBOARD.
- SITE SCRAPE OVER BUILDING AREA TO 10.40.
- CONTOUR LINES AT 200mm INCREMENTS.
- PROVIDE RECYCLED WATER CONNECTION TO ALL WC'S, WM L'DRY POINT AND 2 EXTERNAL HOSE BIB TAPS PROVIDED TO HOUSE LOT.
  RECYCLED TAPS AT METER AND TO SERVICE REAR OF HOUSE.
  PROHIBITION SIGNS TO BE ATTACHED ABOVE TAP ON POST OR WALL AS APPROPRIATE.

LEGEND

SWD	- STORMWATER DRAIN	(E)	- ELECTRICITY PIT
DP	- DOWNPIPE	(SW)	- SW INLET
D	- DRAINS	TBM	- TEMPORARY BENCH MARK
M/B	- METER BOX		
	- PRIVATE OPEN SPACE		

Education use only

SIGNATURE/S

This is the drawing refered to in our contract dated / /

Owner/s

Builder

PROPOSED RESIDENCE FOR OWNER/S

ADDRESS


MAP	JOB NO	DRN

L

TITLE SITE PLAN-SETOUT & LEVELS

SPEC

MST	SCALE 1:200	SHEET 2 OF 12

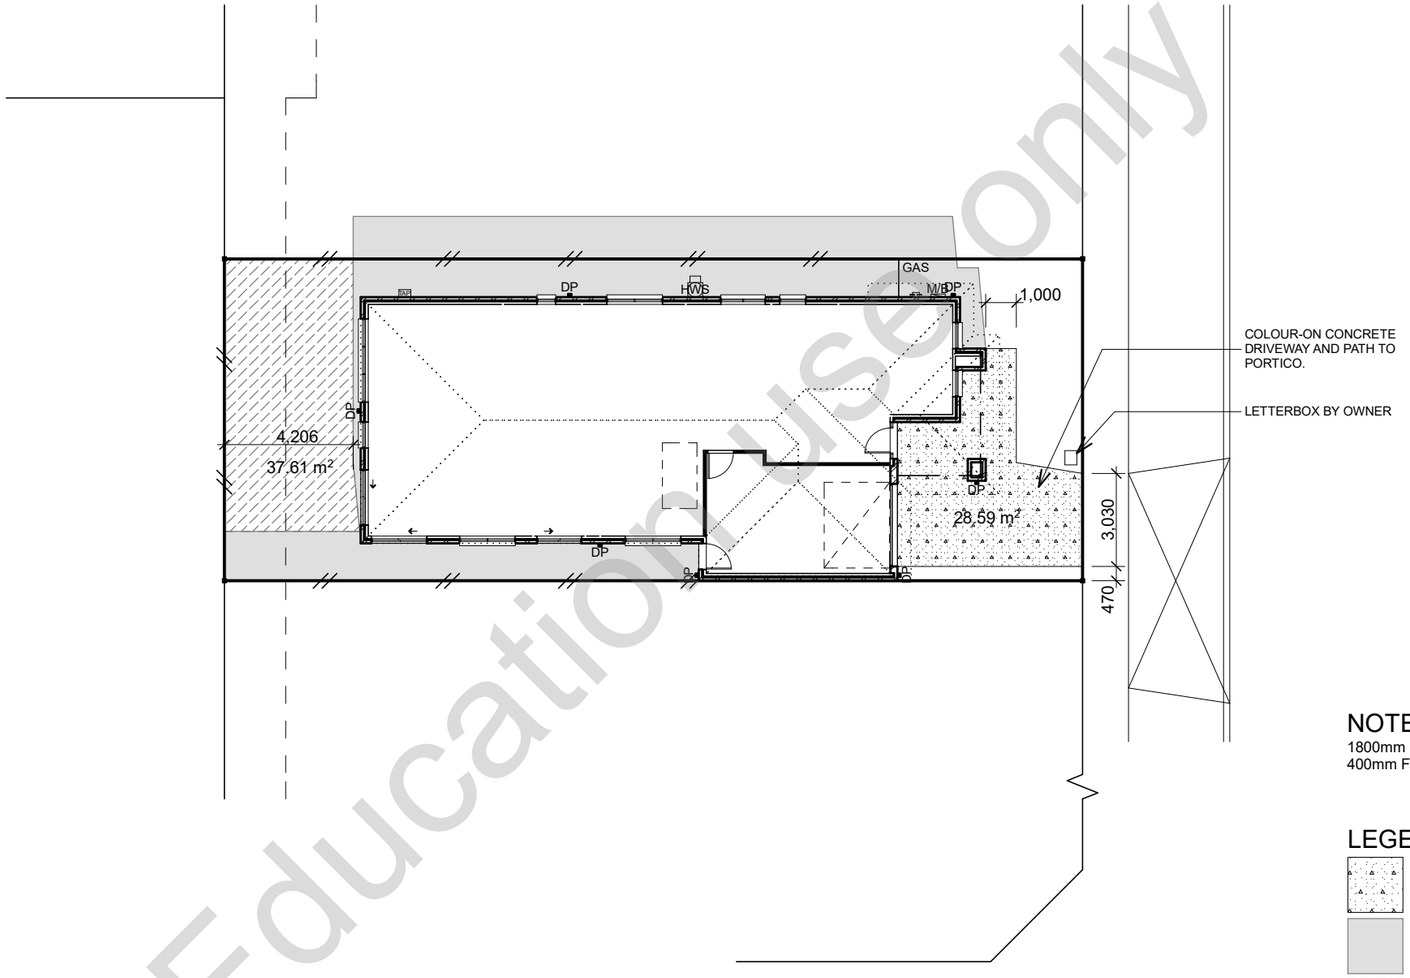

Education use only

NOTE

1800mm HIGH FENCE
400mm FREEBOARD

LEGEND

- DRIVEWAY
- OVERSHADOWING AREA
  SMALL LOT HOUSING CODE: 0.9H
- PRIVATE OPEN SPACE
  WITH DIRECT SUNLIGHT

SITE ANALYSIS

	TOTAL m²	ACTUAL %	MAXIMUM %
LOT SIZE:	294	100	
BUILDING AREA	164.35	55.90	90.00
IMPERMEABLE SURFACE	186.42	63.41	90.00

SIGNATURE/S

This is the drawing refered to in our contract dated / /

Owner/s

Builder

PROPOSED RESIDENCE FOR OWNER/S

ADDRESS


MAP | **JOB NO** | **DRN**

L

TITLE SITE PLAN-GENERAL


SPEC

MST | **SCALE** 1:200 | **SHEET** 3 **OF** 12

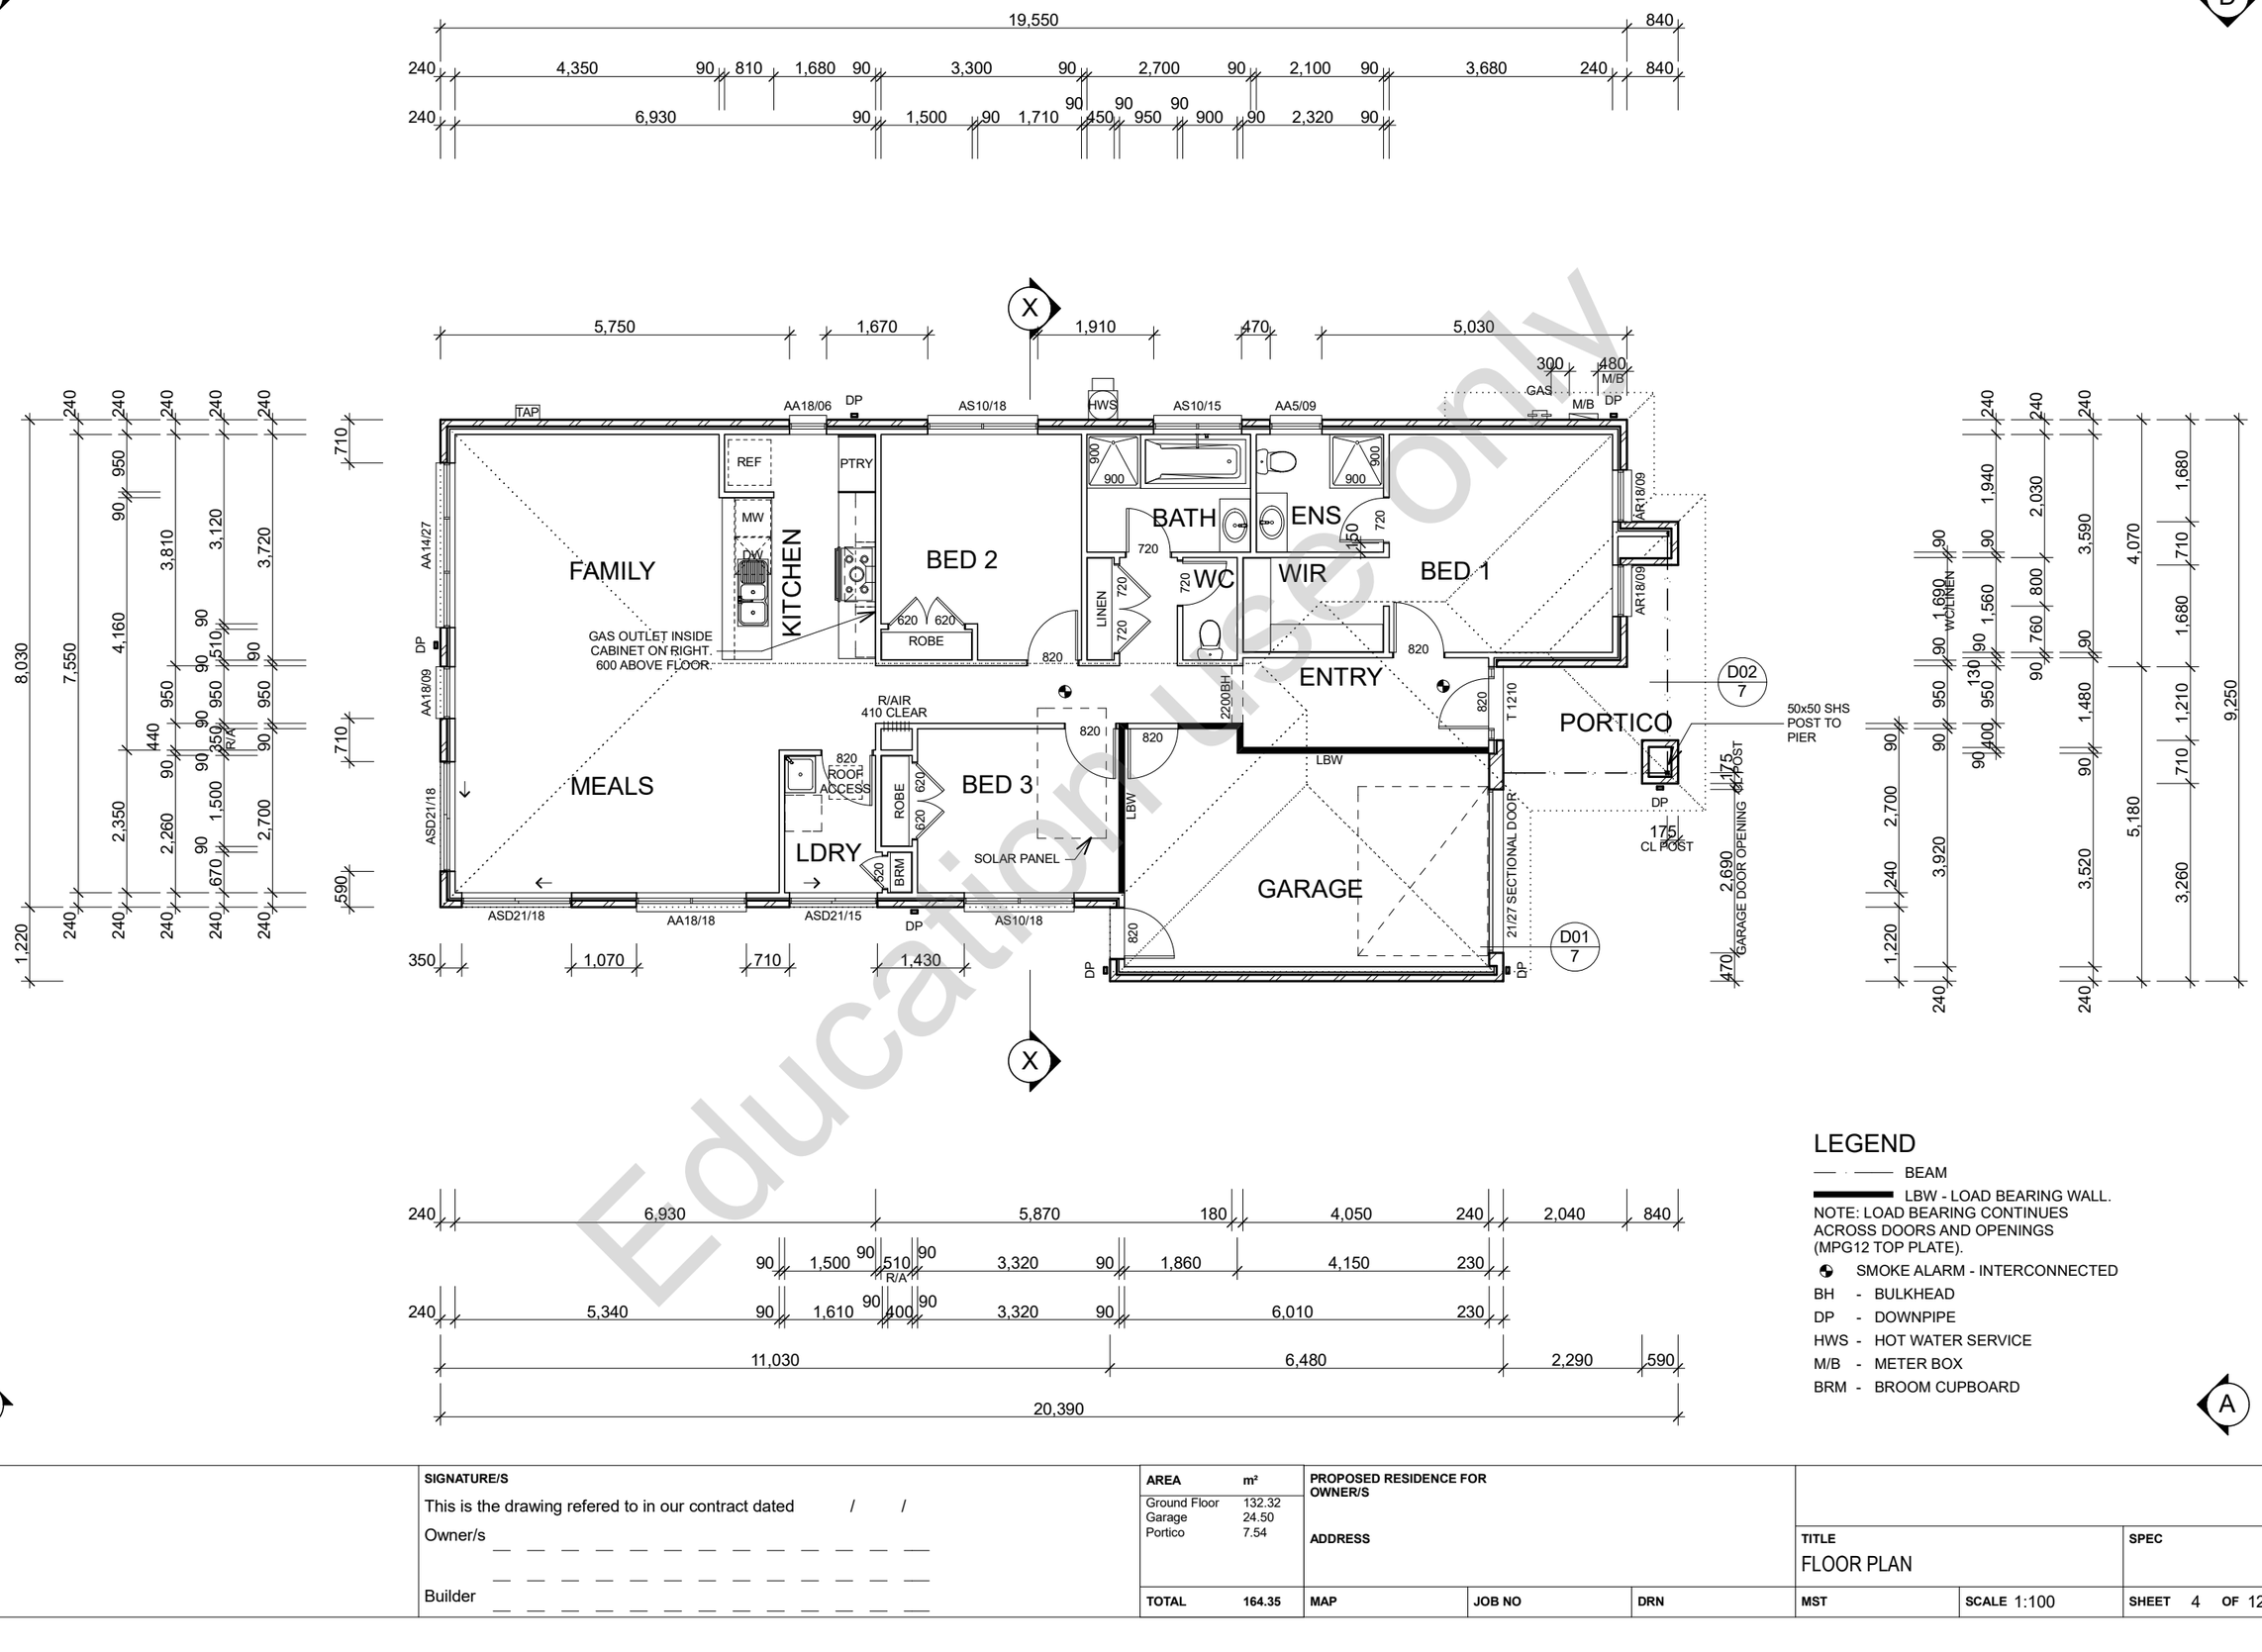


Education Use Only


SIGNATURE/S	**AREA**	**m²**	**PROPOSED RESIDENCE FOR OWNER/S**		L
This is the drawing refered to in our contract dated / /	Ground Floor	132.32			
Owner/s	Garage	24.50	**ADDRESS**		**TITLE** FLOOR PLAN / **SPEC**
Builder	Portico	7.54			
	TOTAL	**164.35**	**MAP** / **JOB NO** / **DRN**	**MST** / **SCALE** 1:100	**SHEET** 4 **OF** 12

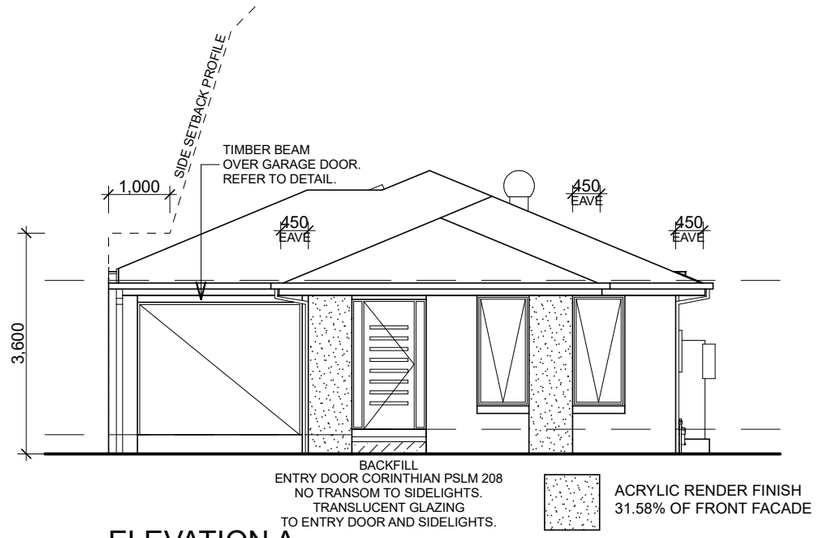

ELEVATION A

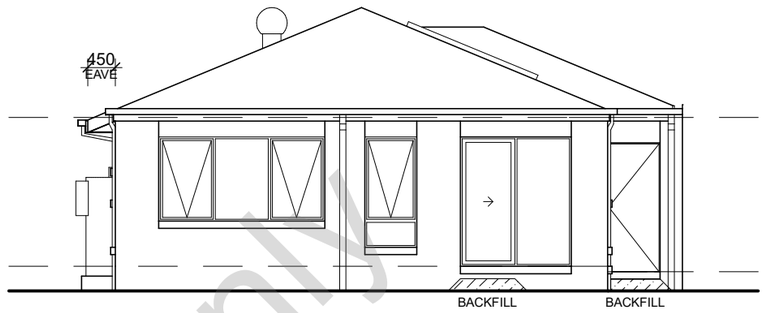


ELEVATION C

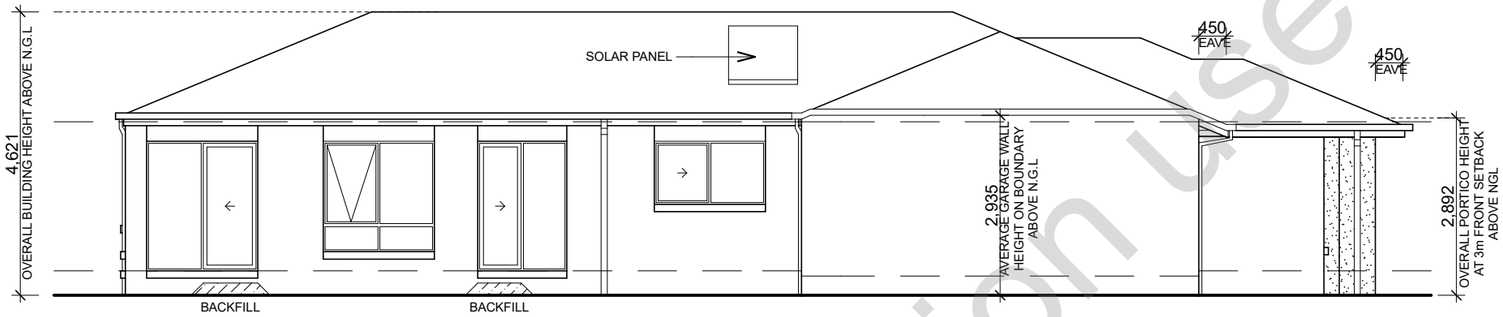

ELEVATION B



RENDER EXTENT PLAN

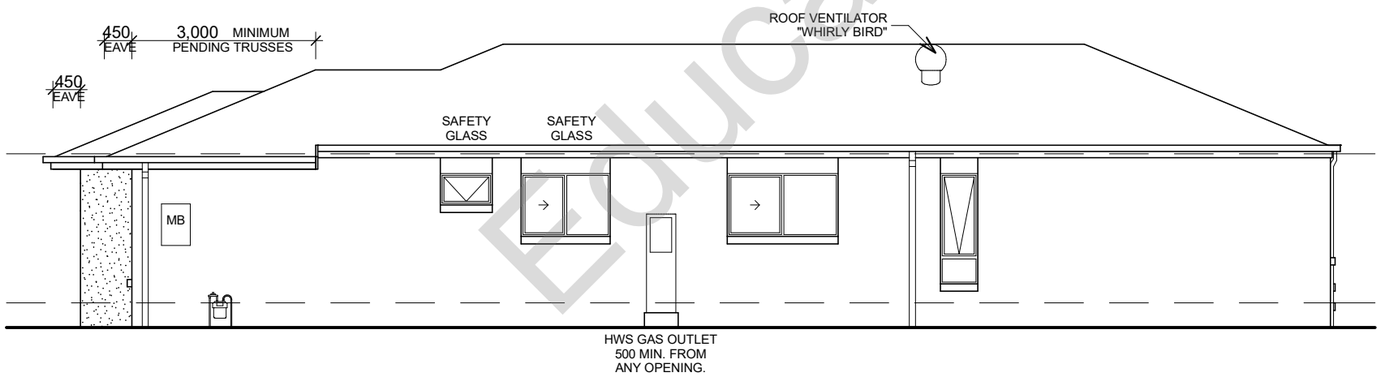


ELEVATION D

WIND RATING N1

- REFER ENGINEERS' DESIGN FOR ARTICULATION JOINTS.
- TOP OF METER BOX 2000mm MAX ABOVE FINISHED GROUND LEVEL.
- WINDOWS TO BE ALUMINIUM, SASHES AS INDICATED.
- SLIDING DOORS TO BE ALUMINIUM, SLIDERS AS INDICATED.
- FC SHEET INFILL OVER EXTERNAL DOORS AND WINDOWS WHERE SHOWN.
- MORTAR JOINTS TO BE FLUSH FINISHED WHERE RENDERED.
- FLY SCREENS TO ALL OPENABLE SASHES.
- WINDOW LOCKS TO ALL OPENABLE SASHES.

Education use only

SIGNATURE/S This is the drawing refered to in our contract dated / / Owner/s Builder	PROPOSED RESIDENCE FOR OWNER/S ADDRESS			L TITLE: ELEVATIONS	SPEC
	MAP	JOB NO	DRN	MST	SCALE 1:100	SHEET 5 OF 12

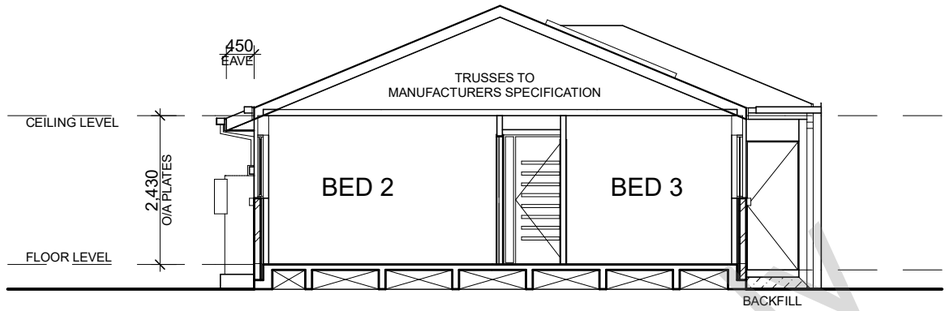


SECTION X

WIND RATING N1
ROOF PITCH 22° 30'

- CONCRETE TILED ROOF WITH TRUSSES AT 600 CTRS.
- PROVIDE 1 No. 300mm ROOF VENT.
- PROVIDE SARKING TO UNDERSIDE OF ROOFING BATTENS.
- WAFFLE RAFT SLAB TO ENGINEERS' DESIGN ON MAXIMUM 50mm CRUSHED ROCK BASE.
- TIMBER FRAMED CONSTRUCTION.

SOIL CLASSIFICATION

SITE IS CLASSIFIED AS CLASS P
AS PER AS 2870.

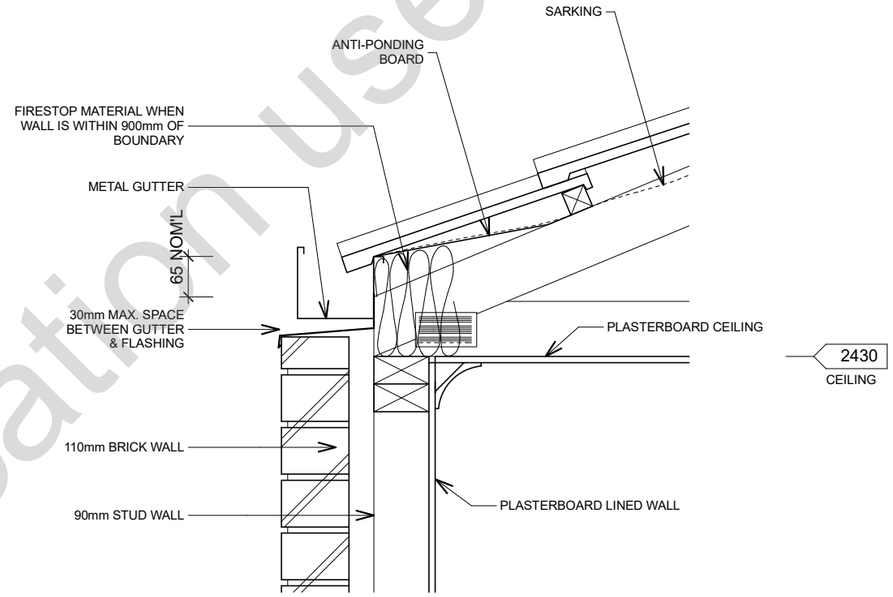


ZERO BOUNDARY GUTTER DETAIL

1 : 10


NO PART OF THE PROPOSED DWELLING
INCLUDING THE FOOTINGS TO PROTRUDE
OVER THE BOUNDARY

Education use only


SIGNATURE/S This is the drawing refered to in our contract dated / / Owner/s Builder	**PROPOSED RESIDENCE FOR OWNER/S** **ADDRESS**		**L**
	MAP	**JOB NO** / **DRN**	**TITLE** SECTION AND DETAIL / **SPEC**
			MST / **SCALE** AS SHOWN / **SHEET** 6 **OF** 12

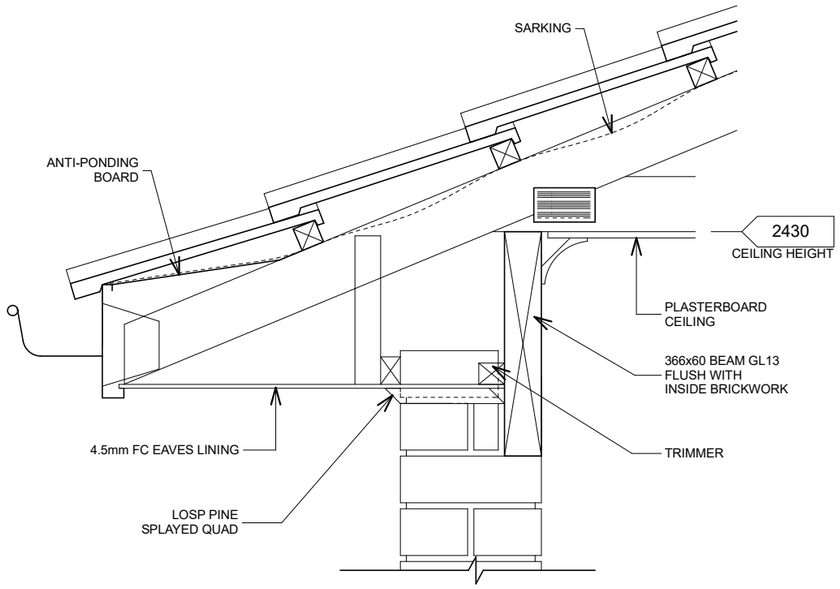


DETAIL 01 - GARAGE BEAM SECTION
1:10

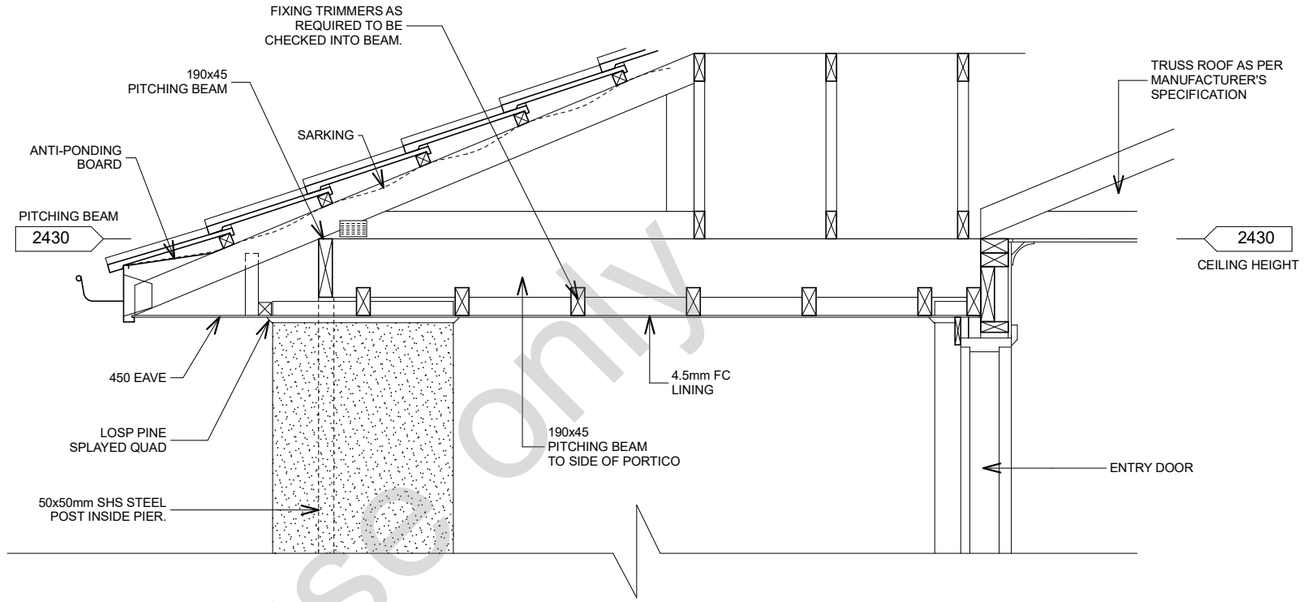

DETAIL 02 - PORTICO
1:20

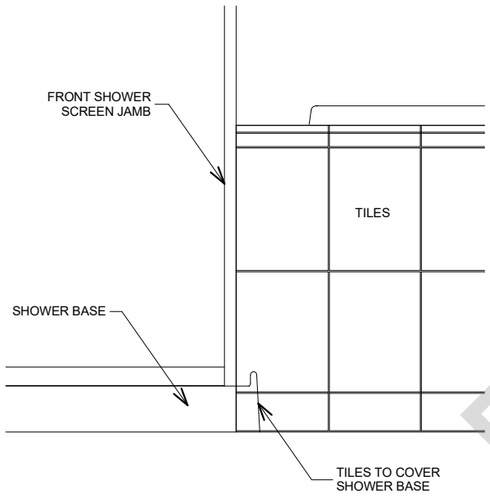

BATH/SHR JUNCTION ELEVATION
1:10

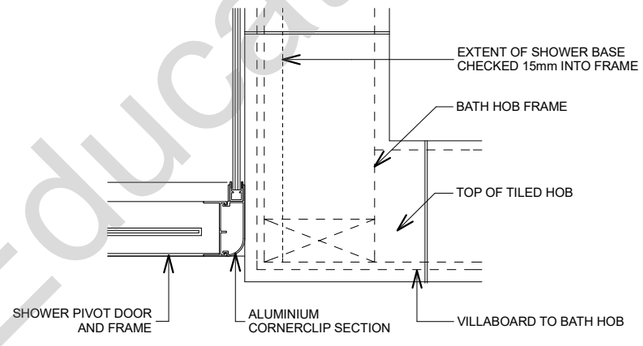



BATH/SHR JUNCTION PLAN
1:5

DENOTES HEIGHT ABOVE HOUSE FL.


Education use only

SIGNATURE/S This is the drawing refered to in our contract dated / / Owner/s Builder	PROPOSED RESIDENCE FOR OWNER/S ADDRESS			MODEL L TITLE DETAILS	SPEC
	MAP	JOB NO	DRN	MST TB 28/08/15 SCALE AS SHOWN	SHEET 7 OF 12

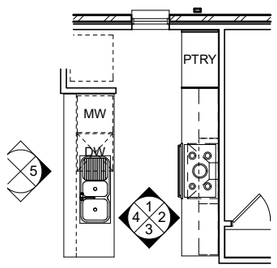


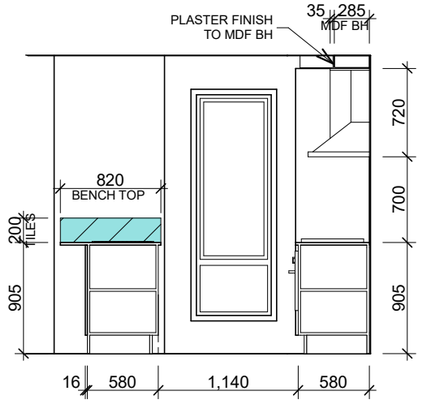


KITCHEN 1

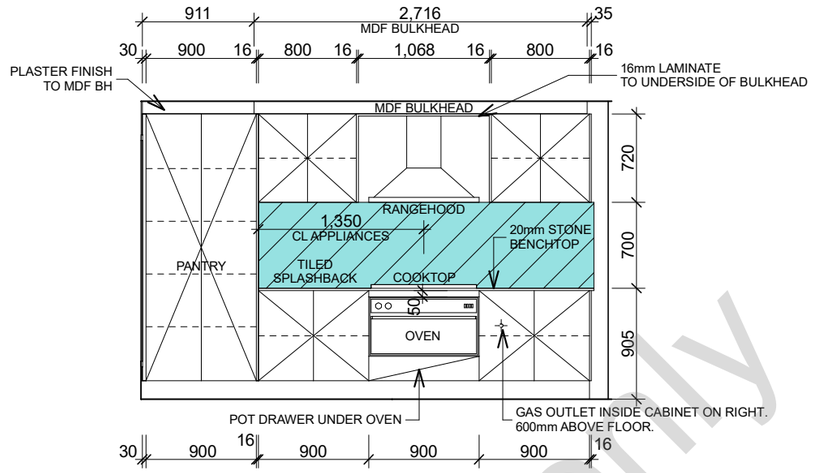


KITCHEN 2

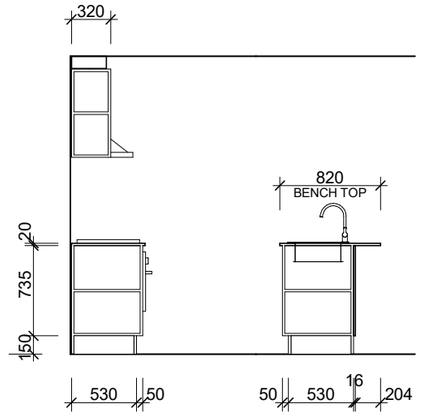


KITCHEN 3

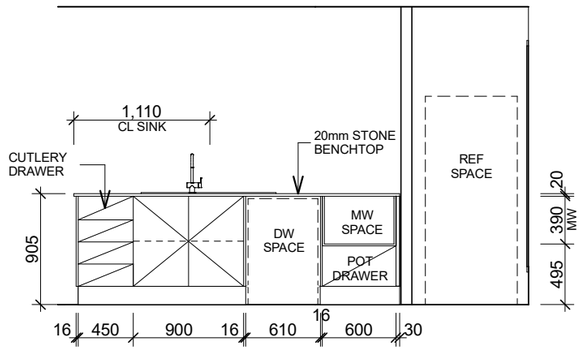


KITCHEN 4

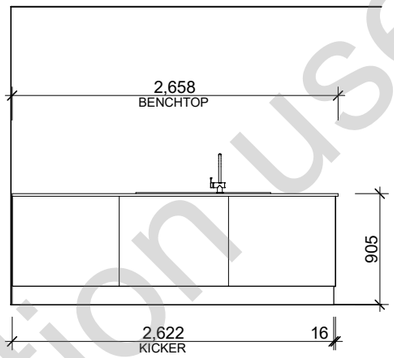


KITCHEN 5

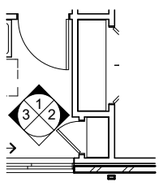


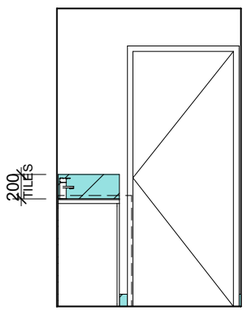

LDRY 1

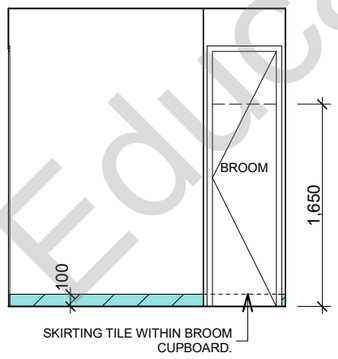

LDRY 2

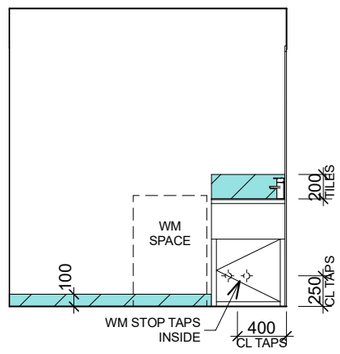

LDRY 3

NOTE

- ALL CABINETRY FIGURES ARE NOMINAL AND MAY DIFFER SLIGHTLY DUE TO DIFFERENT SUPPLIERS. REF SPACES SHOULD BE CONFIRMED ON COMPLETION BY OWNER PRIOR TO PURCHASE.
- ALL APPLIANCES, FITTINGS AND FIXTURES ARE SHOWN AS INDICATIVE ONLY. REFER TO SPECIFICATION FOR MODEL NUMBERS. TO BE INSTALLED AS PER MANUFACTURERS DETAIL AND RECOMMENDATIONS.

Education use only

SIGNATURE/S

This is the drawing refered to in our contract dated / /

Owner/s

Builder

PROPOSED RESIDENCE FOR OWNER/S

ADDRESS


MAP | **JOB NO** | **DRN**


L

TITLE INTERNALS


SPEC

MST | **SCALE** 1:50, 1:100 | **SHEET** 8 **OF** 12

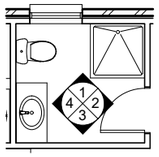


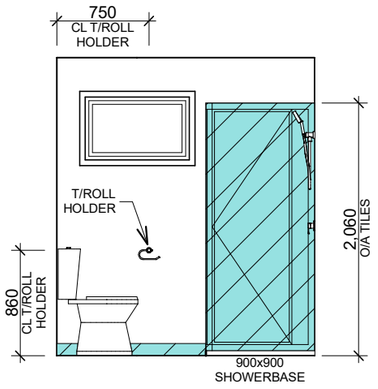


ENSUITE 1

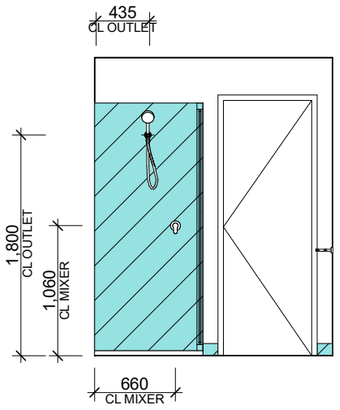


ENSUITE 2

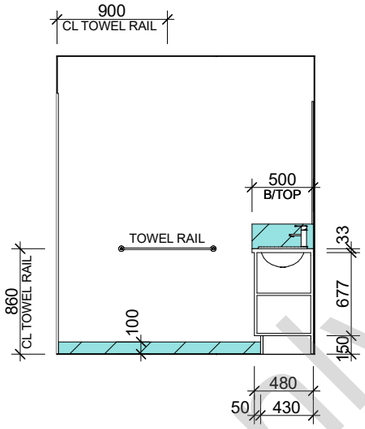


ENSUITE 3

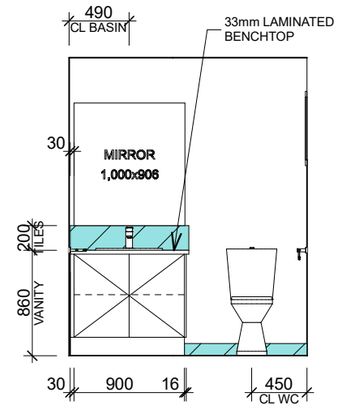


ENSUITE 4

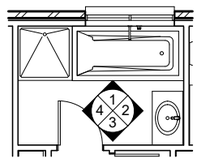


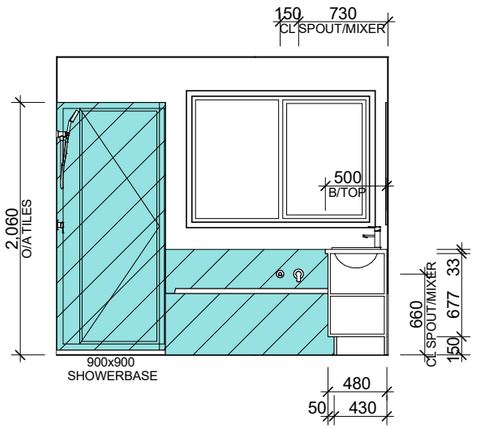


BATH 1

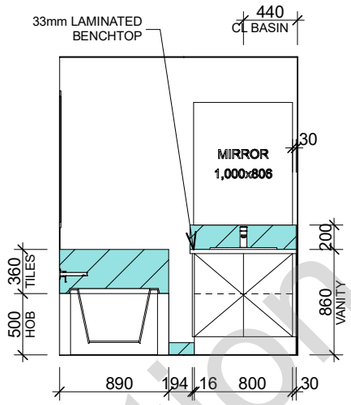


BATH 2

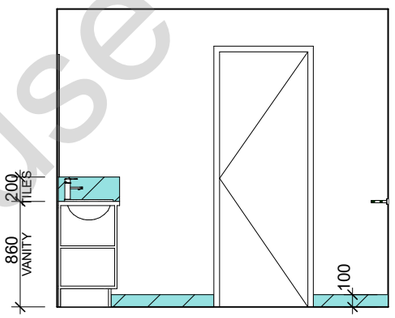


BATH 3

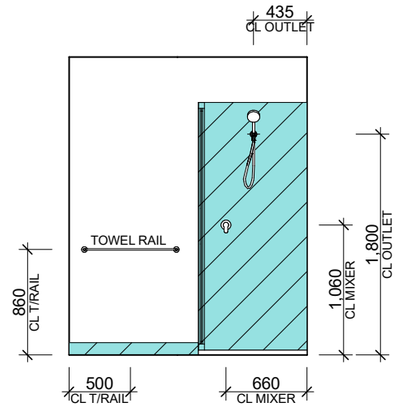


BATH 4

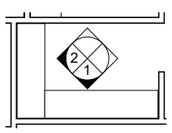


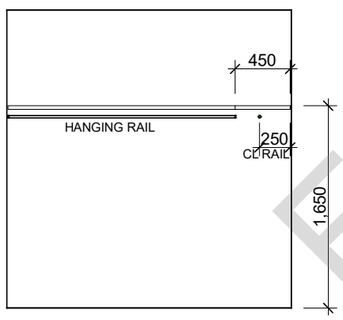


WIR 1

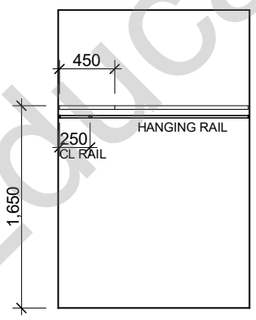

WIR 2

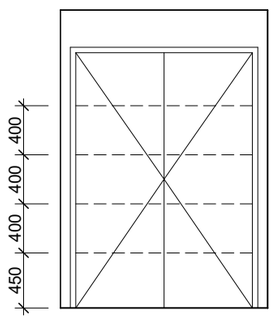

LINEN

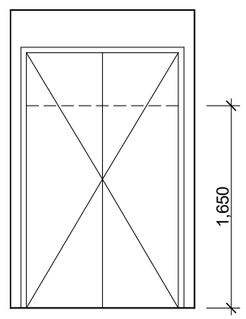

TYPICAL ROBE

NOTE

- ALL CABINETRY FIGURES ARE NOMINAL AND MAY DIFFER SLIGHTLY DUE TO DIFFERENT SUPPLIERS. REF SPACES SHOULD BE CONFIRMED ON COMPLETION BY OWNER PRIOR TO PURCHASE.
- ALL APPLIANCES, FITTINGS AND FIXTURES ARE SHOWN AS INDICATIVE ONLY. REFER TO SPECIFICATION FOR MODEL NUMBERS. TO BE INSTALLED AS PER MANUFACTURERS DETAIL AND RECOMMENDATIONS.

Education use only

SIGNATURE/S

This is the drawing refered to in our contract dated / /

Owner/s

Builder

PROPOSED RESIDENCE FOR OWNER/S


ADDRESS

MAP | **JOB NO** | **DRN**

L

TITLE INTERNALS | **SPEC**

MST | **SCALE** 1:50, 1:100 | **SHEET** 9 **OF** 12

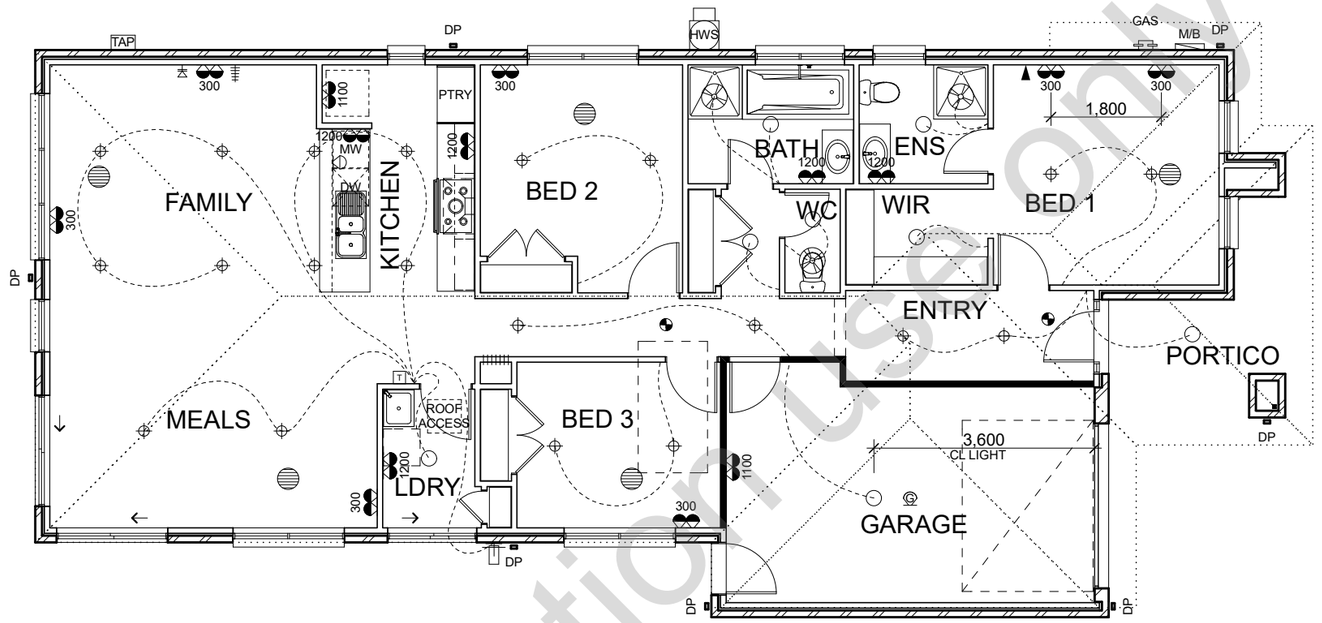

NOTE

- DUCTED HEATING UNIT LOCATED IN ROOF SPACE ADJACENT TO ROOF ACCESS ON PLATFORM, INCL. SPP, GAS POINT AND LIGHT POINT.
- NBN: PLEASE REFER TO NOTE IN CONTRACT.

ELECTRICAL LEGEND

5		Ducted Point - Ceiling
3		Fan - Exhaust
1	HWS	HWS
1		K - Canopy Rangehood
1		K - Cooktop - 900W
1		K - Dishwasher Provision
1		K - Microwave Provision
1		K - Underbench Oven
20		Light - Downlight 240V
8		Light - Point
1		Light Point - Wall Ext.
1		Point - Data
1		Point - Phone
1		Point - TV
14		PP - Double
1		PP - Garage Remote point - (2 Transmitters)
2		Smoke Alarm - Interconnected
1	T	Thermostat

ARTIFICIAL LIGHTING

TO COMPLY WITH N.C.C. 3.12.5.5

	LIGHT TYPE	WATTS PER LIGHT	No.	ADJUSMENT FACTOR	WATTS	TOTAL WATTS	MAX WATTS ALLOWED
INTERNAL HOUSE AREA 5W/m²	BATTEN LIGHTS	9	6	NIL	54	**234.0**	121.69m² x 5W/m² **608**
	DOWN LIGHTS	9	20	NIL	180		
EXTERNAL COVERED AREAS (EXCL. EAVES) 4W/m²	BATTEN LIGHT (PORTICO)	9	1	NIL	9	**9.0**	6.62m² x 4W/m² **26**
GARAGE 3W/m²	BATTEN LIGHT	9	1	NIL	9	**9.0**	24.50m² x 3W/m² **74**

ANY EXTERNAL PERIMETER LIGHTING TO HAVE AN AVERAGE LIGHT EFFICACY OF NOT LESS THAN 40 LUMENS / W.

Education Use only

SIGNATURE/S

This is the drawing refered to in our contract dated / /

Owner/s

Builder

PROPOSED RESIDENCE FOR OWNER/S

ADDRESS


MAP | **JOB NO** | **DRN**

TITLE ELECTRICAL LAYOUT

SPEC

MST | **SCALE** 1:100 | **SHEET** 10 **OF** 12

L

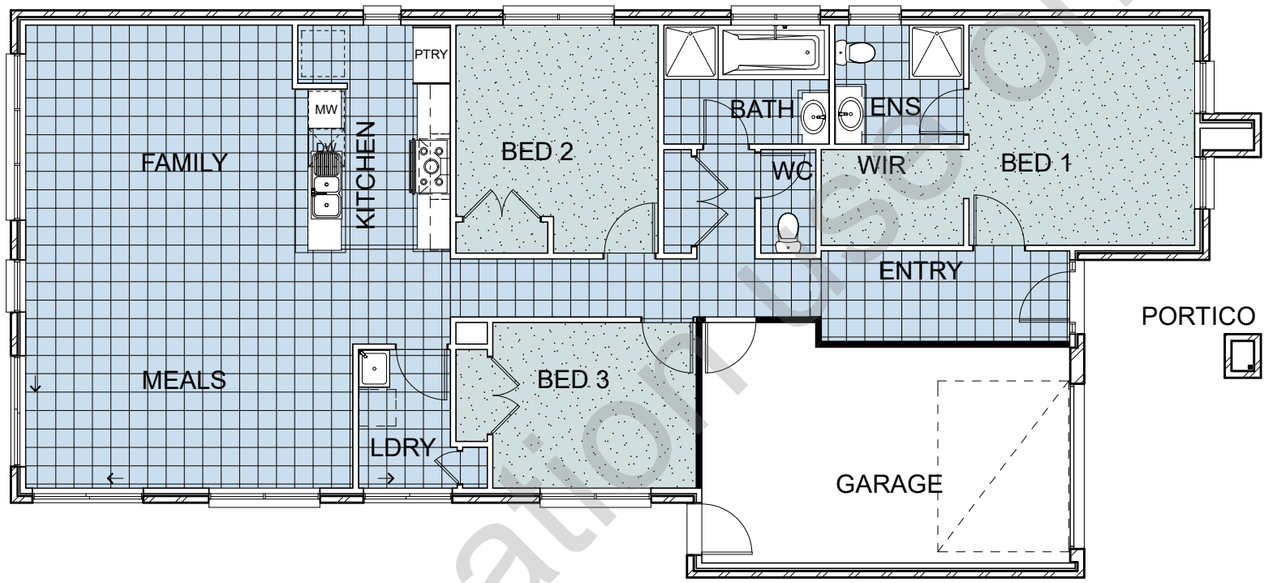

1 - TILED	
KITCHEN	5.5M2
ENS	2.9M2
ENTRY	6.1M2
BATH	2.5M2
LDRY	3.5M2
MEALS/FAMILY	39.9M2
PASSAGE/LINEN	8.6M2
WC	1.5M2
1 - TILED Total:	70.4M2

2 - CARPET	
BED 3	9.8M2
BED 2	12.2M2
BED 1/WIR	17.0M2
2 - CARPET Total:	39.0M2
Grand Total:	109.5M2

FINISHES LEGEND

TILED AREA TO SPECIFICATION.

- PROVIDE SKIRTING TILES TO ALL BUILT IN CUPBOARDS WITHIN WET AREAS.
- FLOOR TILE HATCHING SHOWN INDICATES AREA TO BE TILED ONLY, AND NOT THE FINISHED TILE LAYOUT.
- CONSTRUCTION JOINTS TO BE INSTALLED IN FLOOR TILING EVERY 5m AS PER MANUFACTURES SPECIFICATIONS.

CARPET AREA TO SPECIFICATION.

Education Only

SIGNATURE/S

This is the drawing refered to in our contract dated / /

Owner/s

Builder

PROPOSED RESIDENCE FOR OWNER/S


ADDRESS

MAP | **JOB NO** | **DRN**

TITLE FLOOR FINISHES

SPEC

MST | **SCALE** 1:100 | **SHEET** 11 **OF** 12

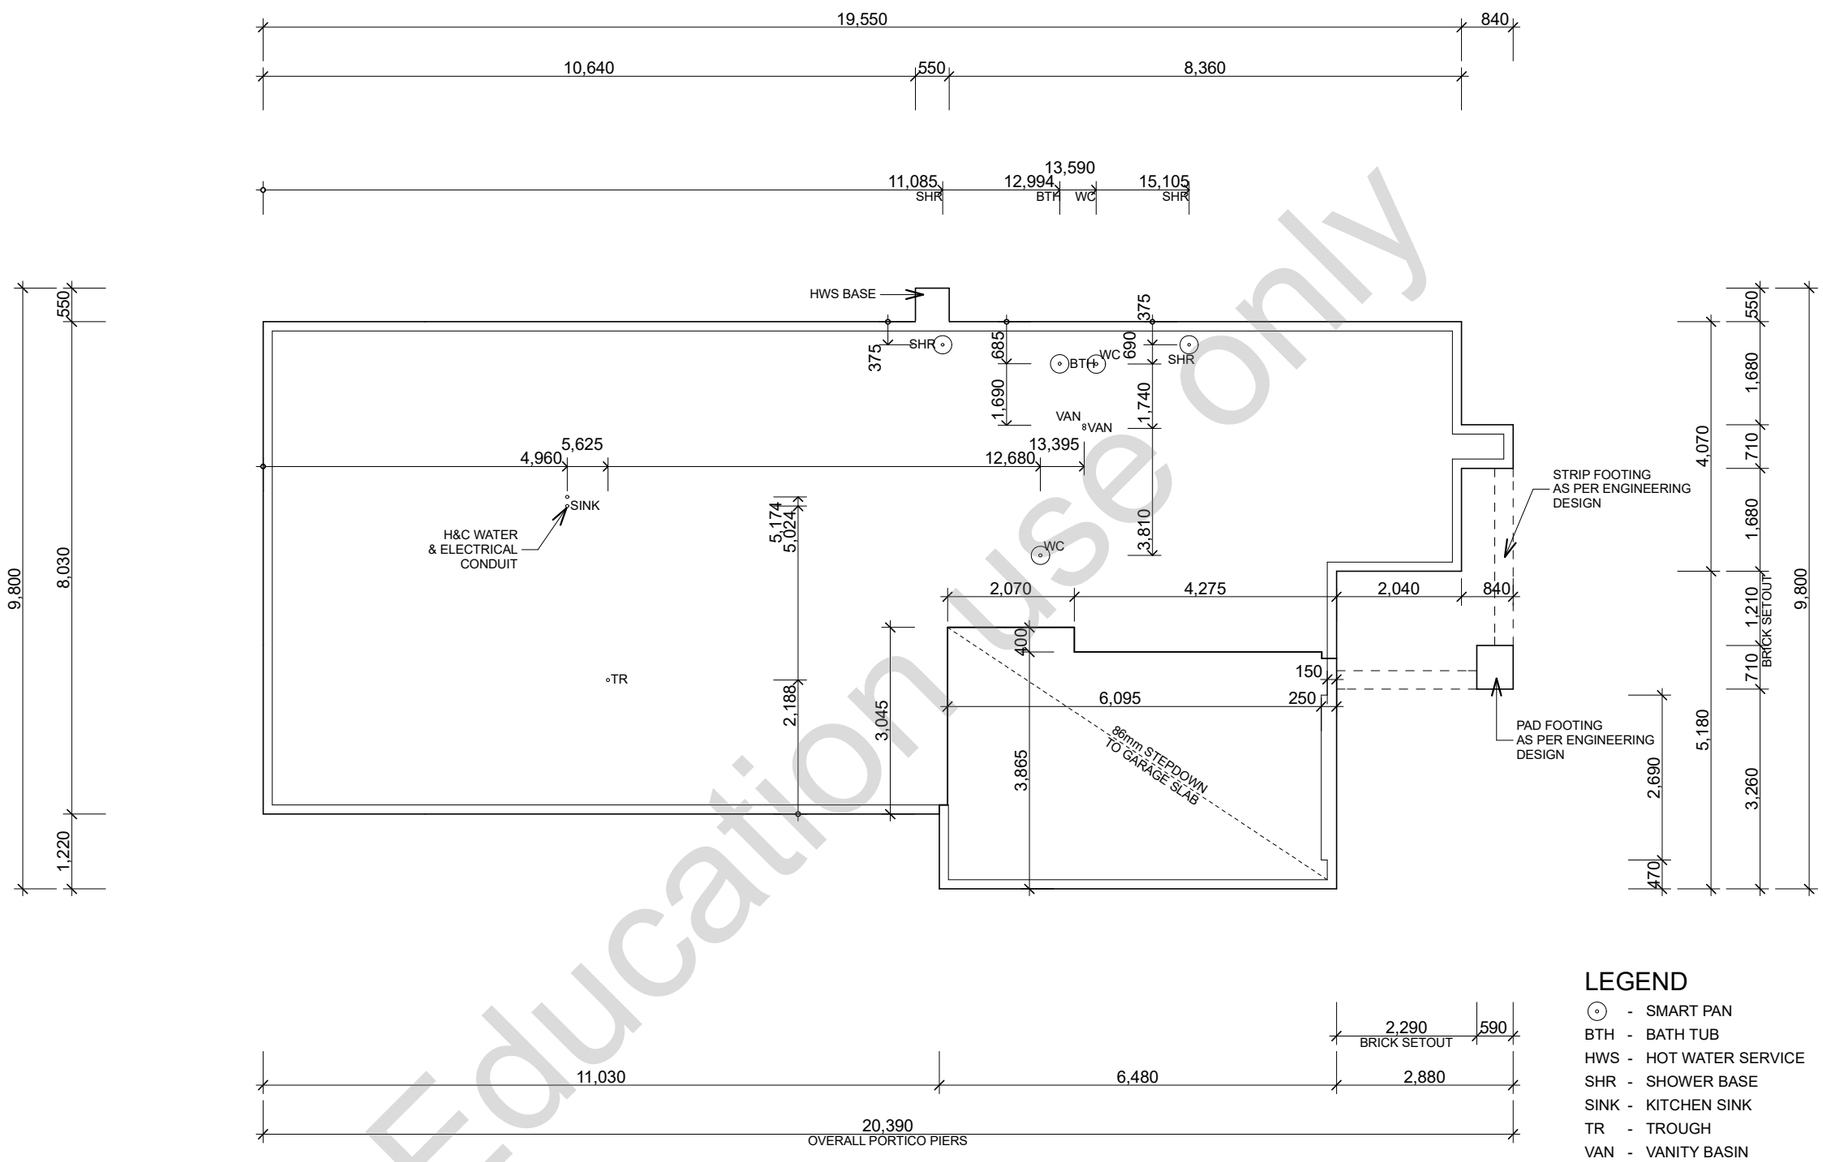

LEGEND

- ◦ - SMART PAN
- BTH - BATH TUB
- HWS - HOT WATER SERVICE
- SHR - SHOWER BASE
- SINK - KITCHEN SINK
- TR - TROUGH
- VAN - VANITY BASIN

Education Use only

SIGNATURE/S	**PROPOSED RESIDENCE FOR OWNER/S**		**L**
This is the drawing refered to in our contract dated / /	**ADDRESS**	**TITLE** SUBFLOOR PLAN	**SPEC**
Owner/s			
Builder	**MAP** / **JOB NO** / **DRN**	**MST** / **SCALE** 1:100	**SHEET** 12 **OF** 12